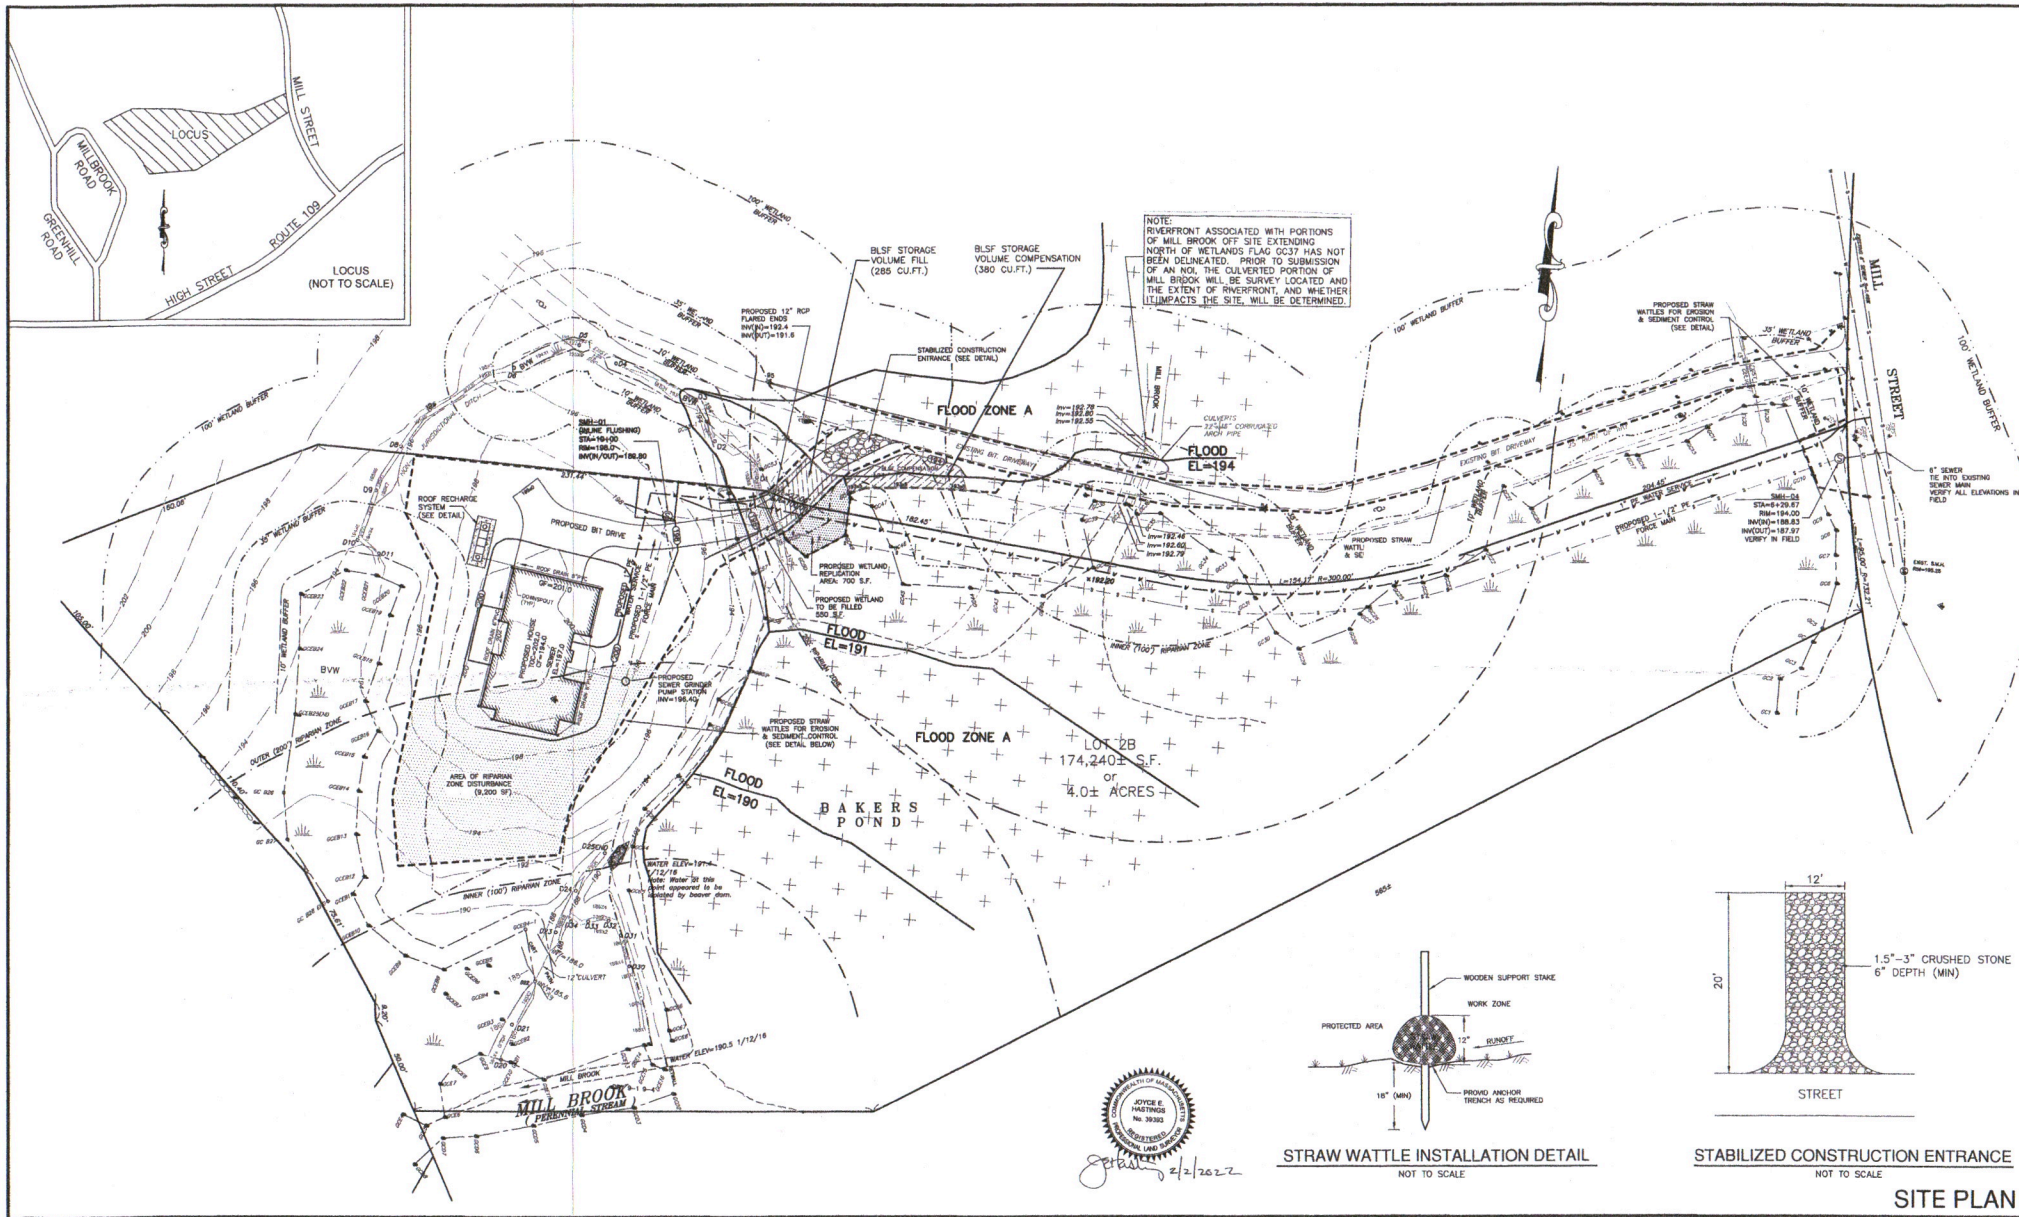


SITE PLAN

NOTE: IT SHALL BE THE RESPONSIBILITY OF THE CONTRACTOR TO VERIFY LOCATIONS AND ELEVATIONS OF EXISTING UTILITIES PRIOR TO COMMENCEMENT OF ANY CONSTRUCTION. DIOSAFE IS TO BE NOTIFIED 72 WORKING HOURS IN ADVANCE OF CONSTRUCTION. DIOSAFE: 1-888-344-7233

REVISIONS		
No.	DATE	DESCRIPTION
1	3/12/2020	FLOOD ZONE
2	12/1/2020	ROOF RECHARGE SYSTEM
3	01/18/21	DRIVEWAY RELOCATION
4	07/01/21	SEWER CONNECTION
5	01/31/22	FLOOD COMPENSATION

FLD. BY OTHERS: DRW. CHKD. PC

GRAPHIC SCALE

(IN FEET)
1 inch = 30 ft.

GLM Engineering Consultants, Inc.
19 EXCHANGE STREET
HOLLISTON, MA 01746
P: 508-429-1100 F: 508-429-7160
www.GLMengineering.com

PROPOSED SITE PLAN OF LAND LOT 2B - MILL STREET WESTWOOD, MASSACHUSETTS

PREPARED FOR:
SALVATORE VINCI
65 BAY COLONY DRIVE
WESTWOOD, MA 02090

JOB No. 11,074
DATE: NOV 2, 2018
SCALE: 1"=30'
SHEET: 1 OF 3
PLAN #: 27,465

February 25, 2022

MassDEP Northeast Regional Office
205B Lowell Street
Wilmington, MA 01887

Re: BLSF Cut/Fill Chart- Superseding Order of Conditions
42 Mill St., Westwood, MA (DEP #438-0706)

MassDEP Northeast Regional Office:

Goddard Consulting, LLC is pleased to submit this BLSF cut & fill chart requested by MassDEP, associated with the request for a Superseding Order of Conditions (SOC) on behalf of the applicant, Joanne Delapa, Delapa Realty Trust. See table below:

Elevation	Fill	Cut (Compensatory)	Incremental Increase
193.5- 194	285cf	380cf	+95cf

If there are any questions concerning this information, please do not hesitate to contact us.

Sincerely,

Goddard Consulting, LLC



Scott Goddard, Principal & PWS
Professional Wetland Scientist