


REGISTRY USE ONLY

ENDORSEMENT OF THIS PLAN DOES NOT
CONSTITUTE AN INTERPRETATION OF ZONING

APPROVAL UNDER SUBDIVISION
CONTROL LAW NOT REQUIRED.


WESTWOOD PLANNING BOARD

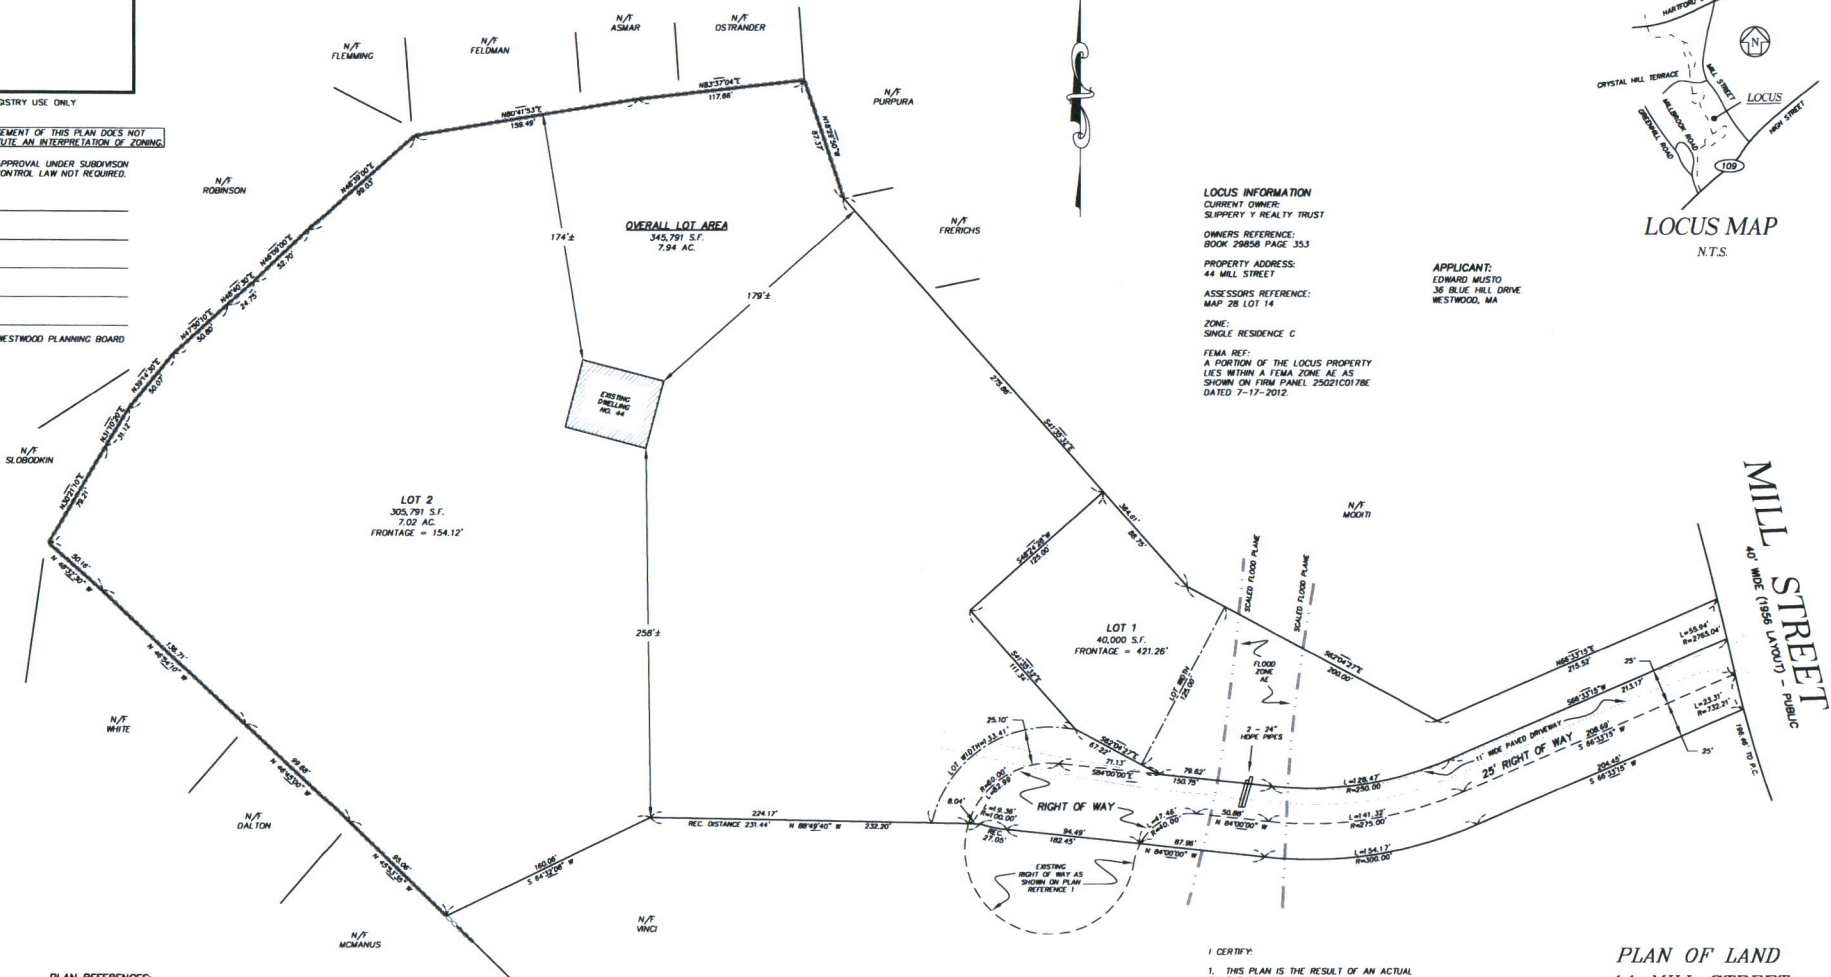

LOCUS INFORMATION
CURRENT OWNERS:
SLIPPERY T REALTY TRUST
OWNERS REFERENCE:
BOOK 29858 PAGE 35.3
PROPERTY ADDRESS:
44 MILL STREET
ASSESSORS REFERENCE:
MAP 28 LOT 14
ZONE:
SINGLE RESIDENCE C

FEMA REF:
A PORTION OF THE LOCUS PROPERTY
LIES WITHIN A FEMA ZONE AE AS
SHOWN ON FIRM PANEL 25021C0178E
DATED 7-17-2012.

APPLICANT:
EDWARD MUSTO
36 BLUE HILL DRIVE
WESTWOOD, MA

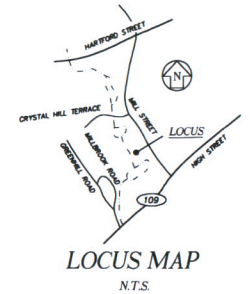

MILL STREET
40' WIDE (1956 LAYOUT) - PUBLIC

PLAN REFERENCES:
1. BOOK 4294 PAGE 671
2. BOOK 4240 PAGE 193
3. BOOK 211 PAGE 616
4. BOOK 3801 PAGE 385
5. BOOK 4405 PAGE 736
6. BOOK 201 PAGE 291-292

I CERTIFY:
1. THIS PLAN IS THE RESULT OF AN ACTUAL
ON THE GROUND SURVEY.
2. THAT THIS PLAN WAS PREPARED IN
CONFORMANCE WITH THE RULES AND
REGULATIONS OF THE REGISTERS OF DEEDS.

PLAN OF LAND
44 MILL STREET
WESTWOOD, MASSACHUSETTS
SCALE 1" = 40' DATE: JANUARY 20, 2016

PETER G. HOYT P.L.S. DATE

HOYT LAND SURVEYING
1287 WASHINGTON STREET
WEYMOUTH MA. 02189
781-682-9192